


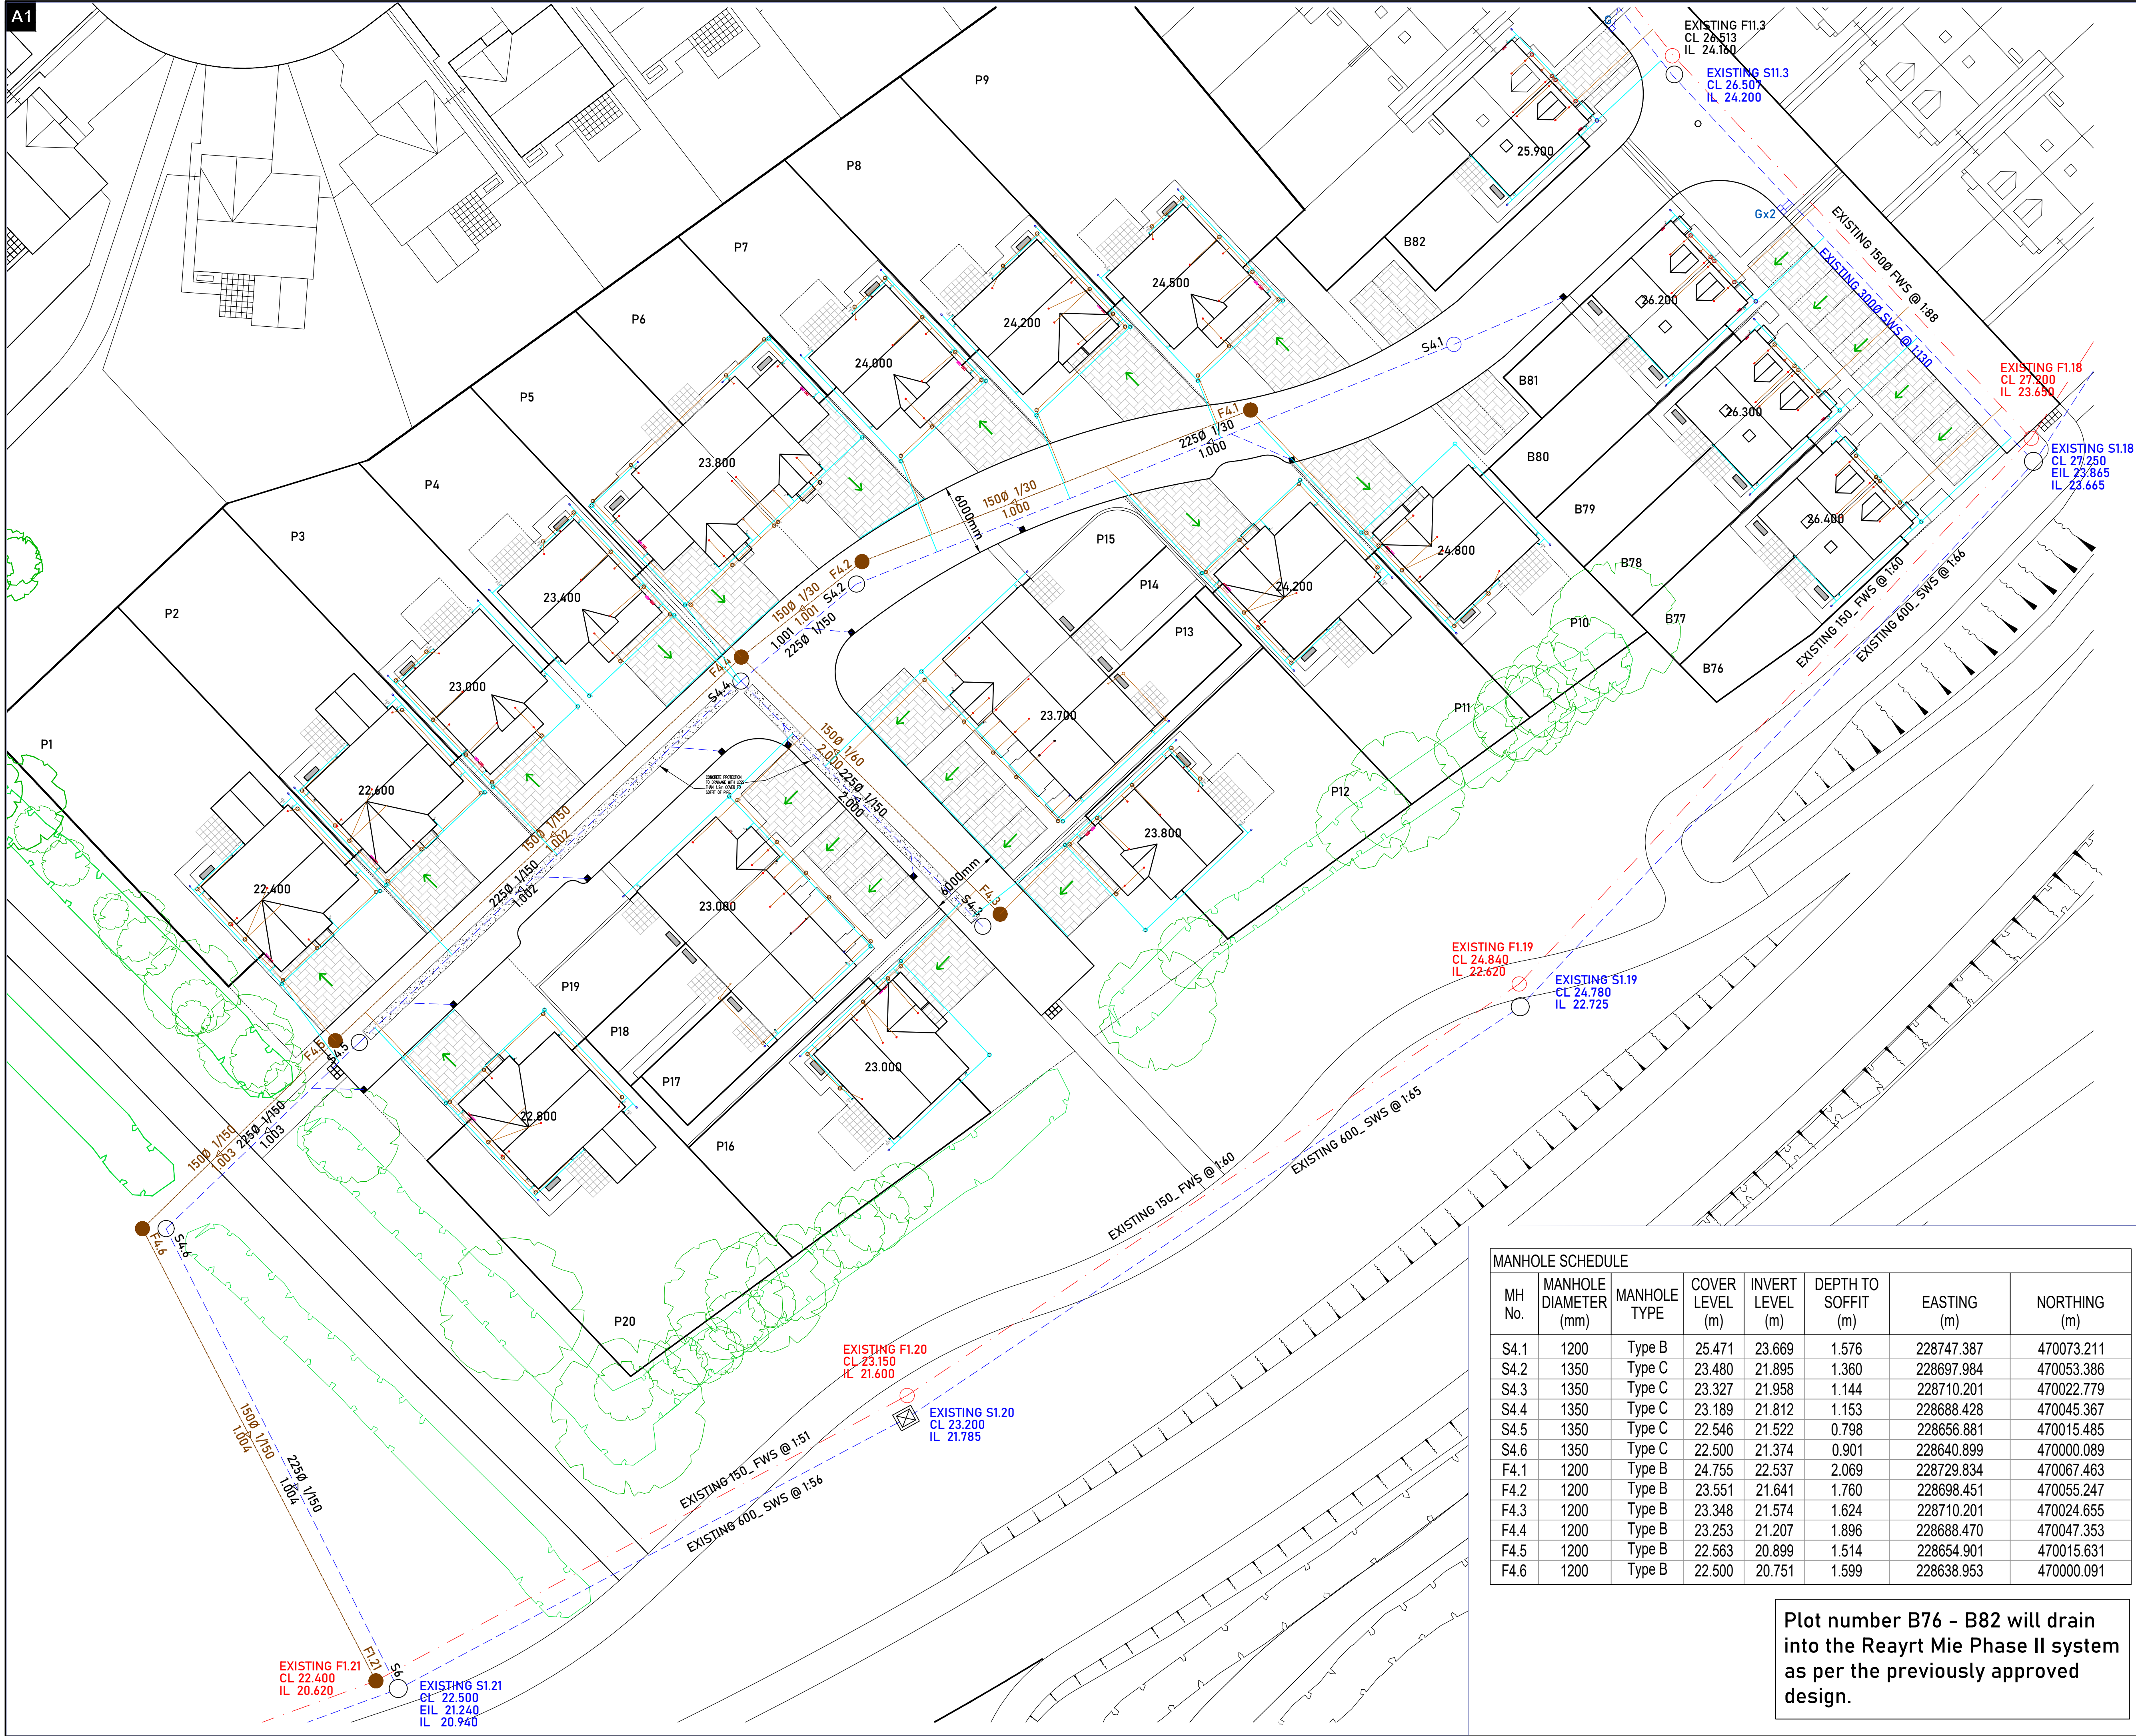

NOTES.

P02	Issued for Section 4 & Section 8 Agreement	09.12.2025	MS
REV.	AMENDMENT	DATE	BY

dandara

Dandara Group Head Office
Isle of Man Business Park
Coolil Road, Braddan
Isle of Man
IM2 2SA
Tel: 01624 693300 Email: isleofman@dandara.com Web: www.dandara.com

CLIENT:
Dandara Homes Ltd

DRAWING:
Drainage Layout

STATUS:
Approval

SCALE:
1:100

JOB No:
2333

DRAWING No.:
2333-DAN-BA4-DR-D-C-90001

DATE:
December 2025

NAME:
MS / MK

Rev
P02

MANHOLE SCHEDULE

MH No.	MANHOLE DIAMETER (mm)	MANHOLE TYPE	COVER LEVEL (m)	INVERT LEVEL (m)	DEPTH TO SOFFIT (m)	EASTING (m)	NORTHING (m)
S4.1	1200	Type B	25.471	23.669	1.576	228747.387	470073.211
S4.2	1350	Type C	23.480	21.895	1.360	228697.984	470053.386
S4.3	1350	Type C	23.327	21.958	1.144	228710.201	470022.779
S4.4	1350	Type C	23.189	21.812	1.153	228688.428	470045.367
S4.5	1350	Type C	22.546	21.522	0.798	228656.881	470015.485
S4.6	1350	Type C	22.500	21.374	0.901	228640.899	470000.089
F4.1	1200	Type B	24.755	22.537	2.069	228729.834	470067.463
F4.2	1200	Type B	23.551	21.641	1.760	228698.451	470055.247
F4.3	1200	Type B	23.348	21.574	1.624	228710.201	470024.655
F4.4	1200	Type B	23.253	21.207	1.896	228688.470	470047.353
F4.5	1200	Type B	22.563	20.899	1.514	228654.901	470015.631
F4.6	1200	Type B	22.500	20.751	1.599	228638.953	470000.091

Plot number B76 - B82 will drain into the Reayrt Mie Phase II system as per the previously approved design.