


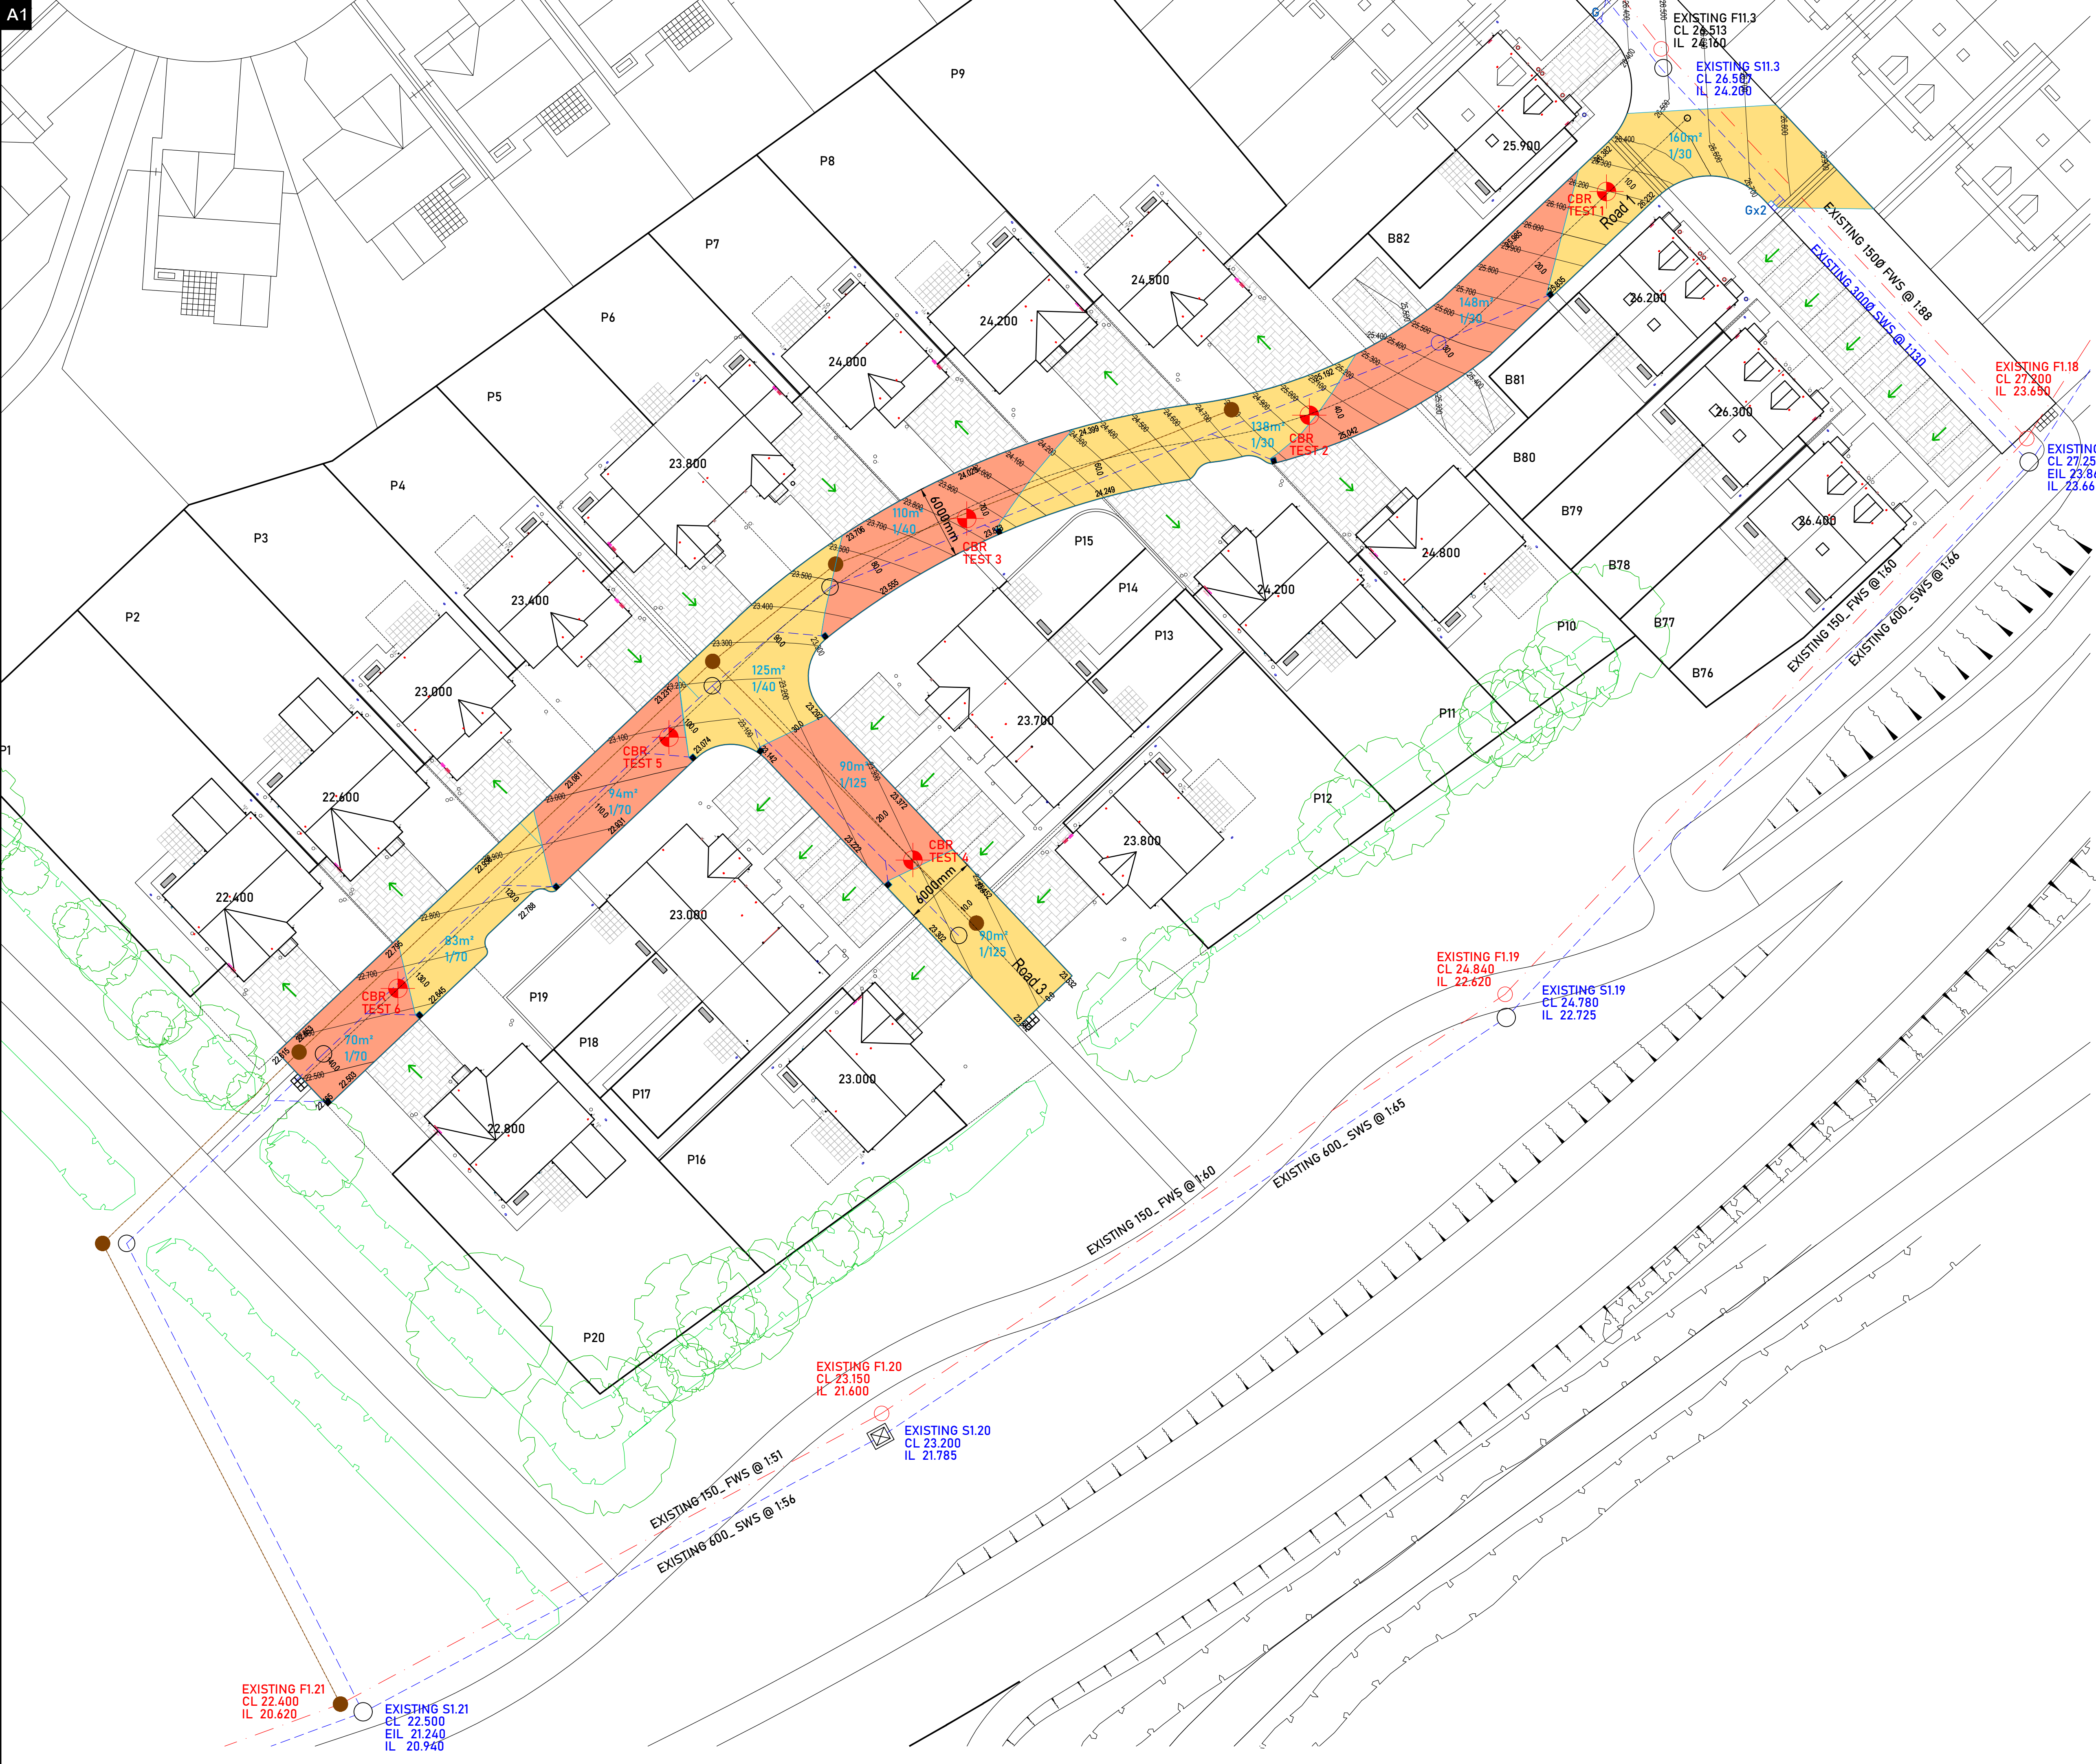

NOTES.

P02	Issued for Section 4 & Section 8 Agreement	09.12.2025	MS
REV.	AMENDMENT	DATE	BY
dandara Dandara Group Head Office Isle of Man Business Park Cool Road, Braddan Isle of Man IM2 2SA Tel: 01624 693300 Email: isleofman@dandara.com Web: www.dandara.com			
CLIENT: Dandara Homes Ltd			
PROJECT: Parkfield Ballahick Lane Ballasalla			
DRAWING: Road Layout and Gulley Drainage Areas			
STATUS: Approval			
SCALE: 1:100		DATE: December 2025	
JOB No.: 2333		NAME: MS / MK	
DRAWING No.: 2333-DAN-BA4-DR-D-C-90002			Rev P02