
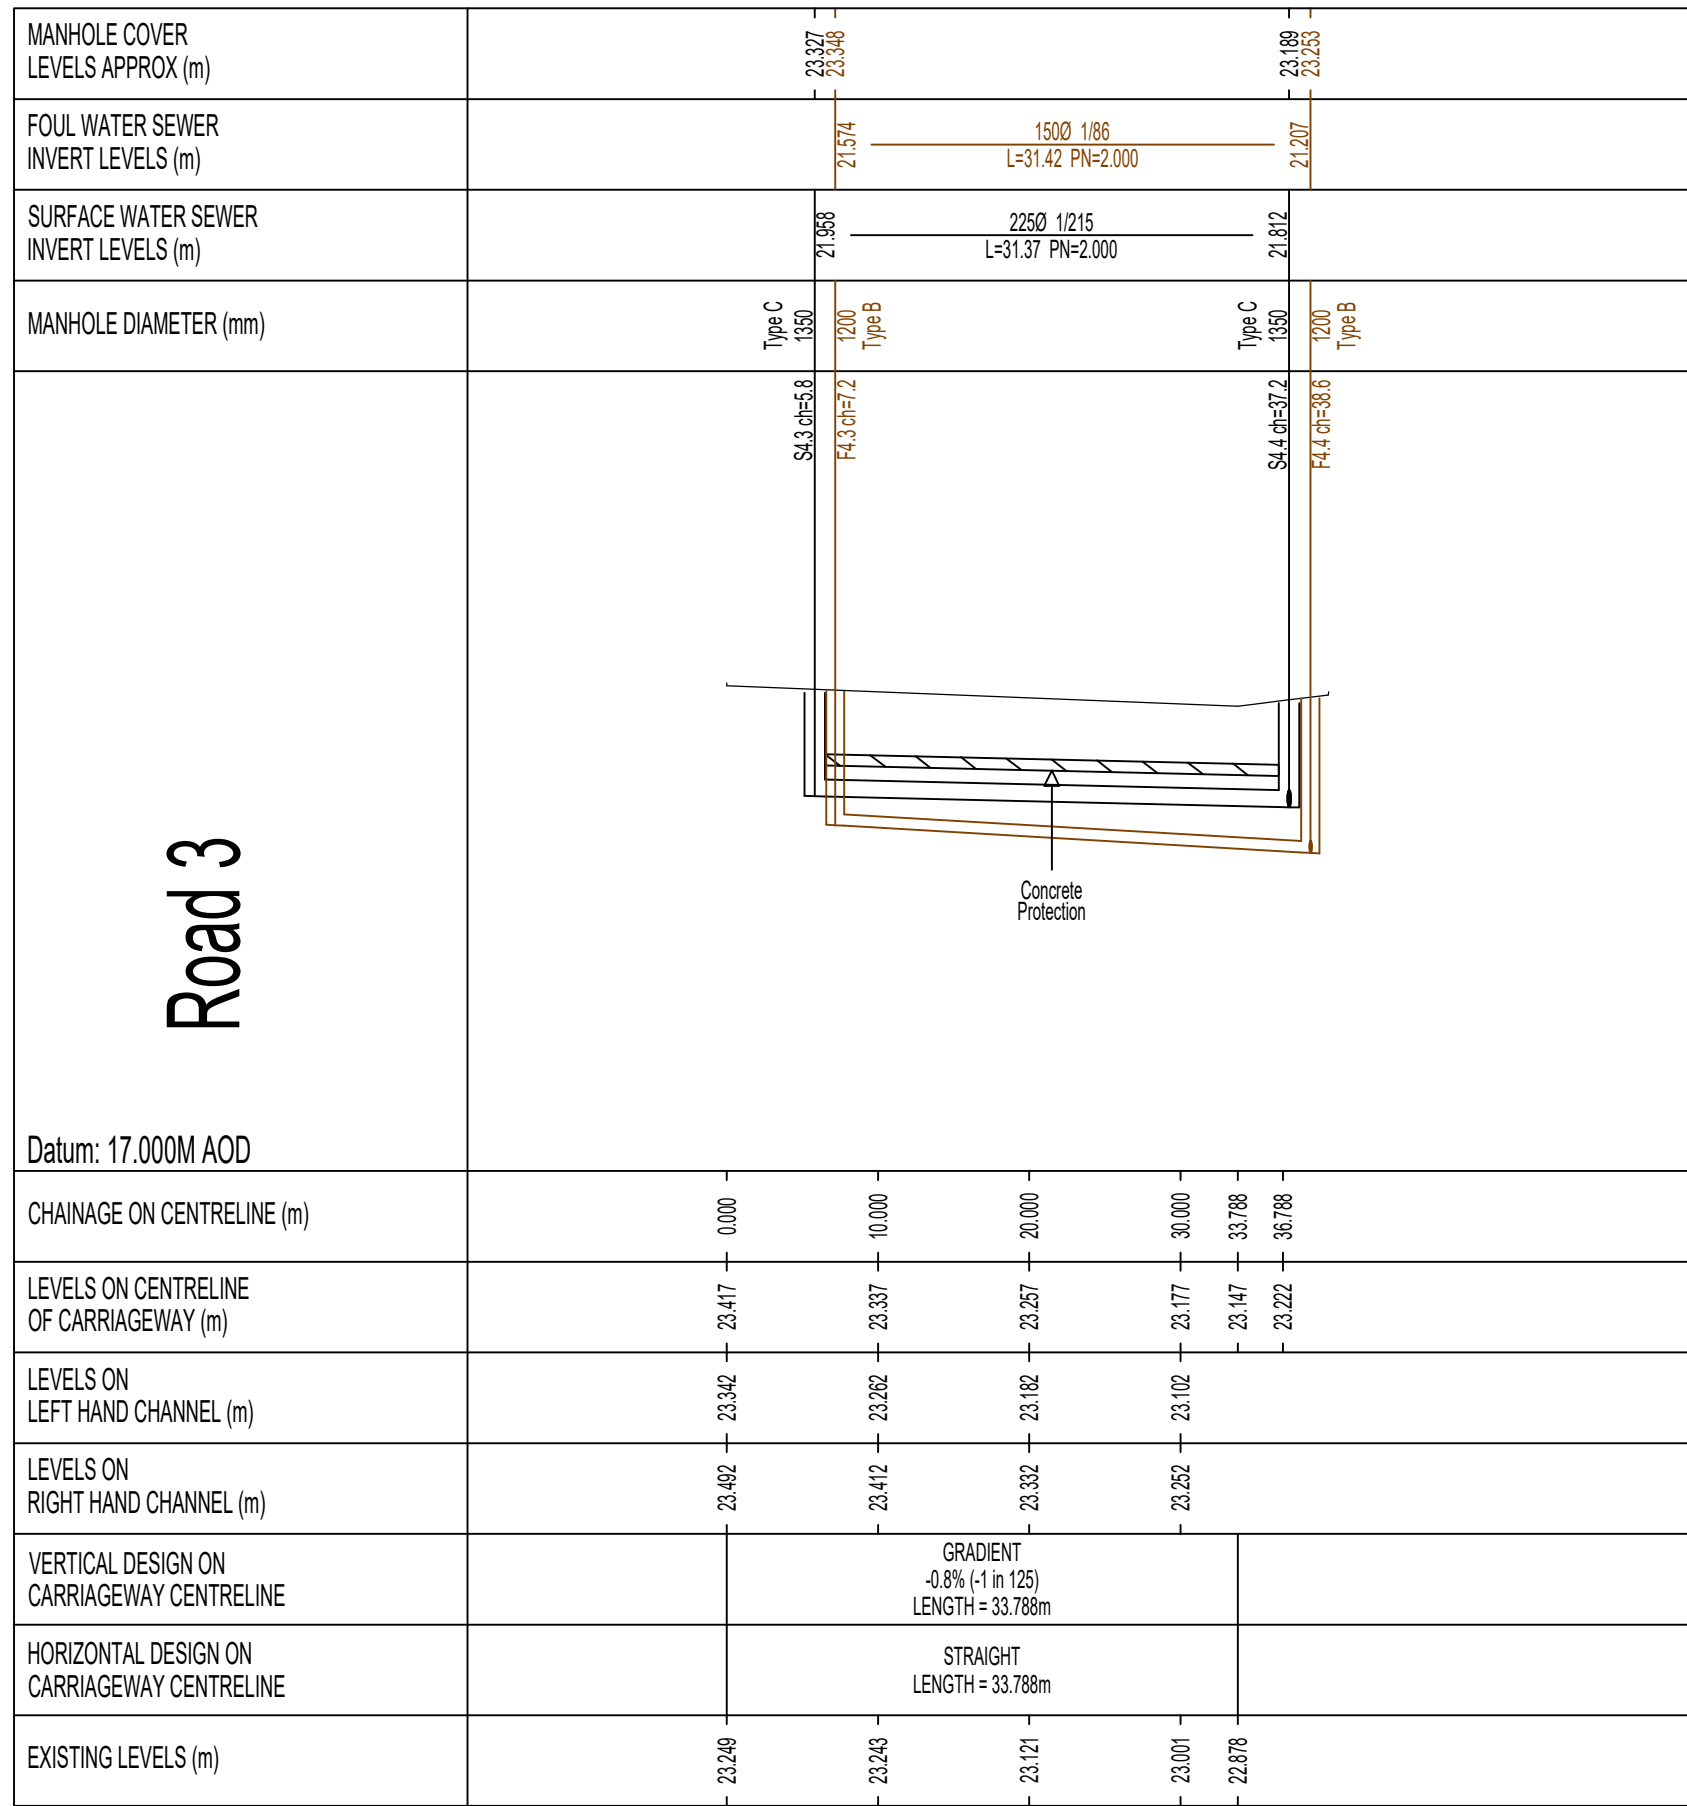


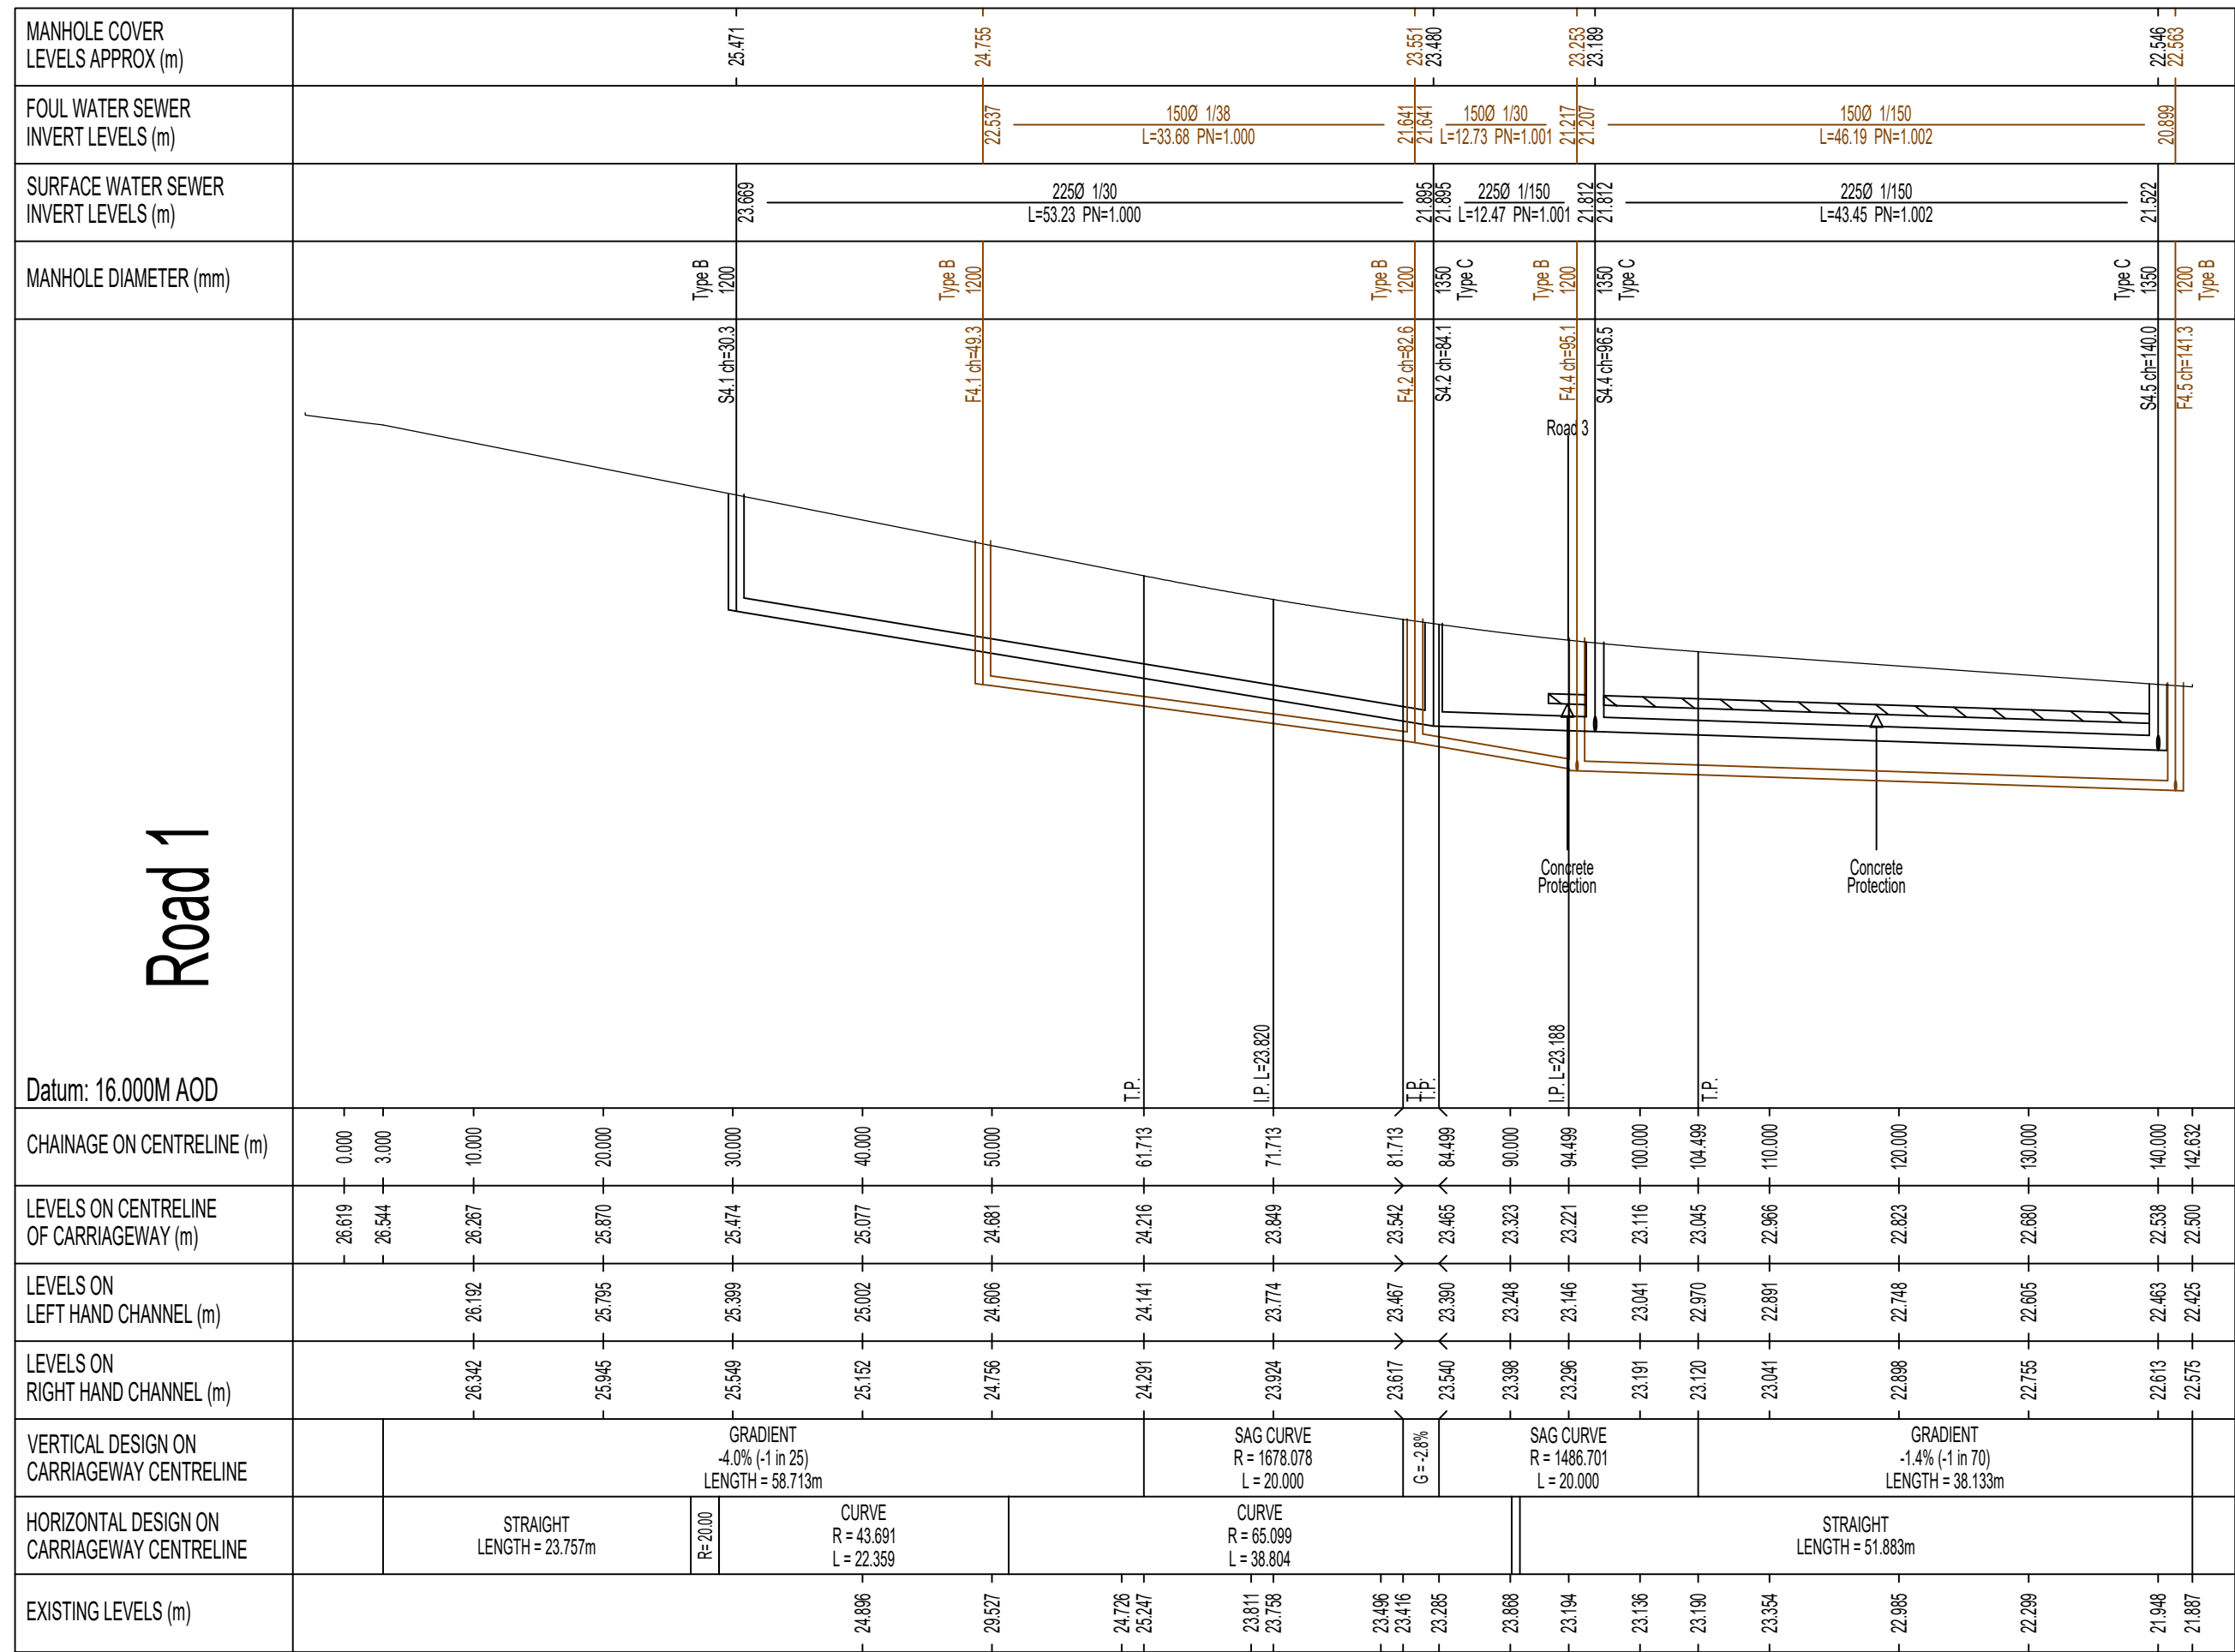

NOTES.

This drawing and the copyright remain the property of Dandara Homes Limited.
It may not be copied or altered without their written permission and must be returned to the Housing Department when work is completed.
All dimensions must be checked on site. Any discrepancies should be notified to the Architects. Only written dimensions shall be followed.

This drawing MUST be read with other Architectural and Engineers drawings and the specification.

P01	Issued for Section 4 & Section 8 Agreement	09.12.2025	MS
REV.	AMENDMENT	DATE	BY
 dandara Dandara Group Head Office Isle of Man Business Park Coolil Road, Braddan Isle of Man IM2 2SA Tel: 01624 693300 Email: isleofman@dandara.com Web: www.dandara.com			
CLIENT:			
Dandara Homes Ltd			
PROJECT:			
Parkfield Ballahick Lane Ballasalla			
DRAWING:			
Road Longitudinal Sections			
STATUS:			
Approval			
SCALE:		DATE:	
1:500 H, 1,100 V		December 2025	
JOB NO:		NAME:	
2333		MS	
DRAWING: 2333-DAN-BA4-DR-D-C-90006			Rev: P01