


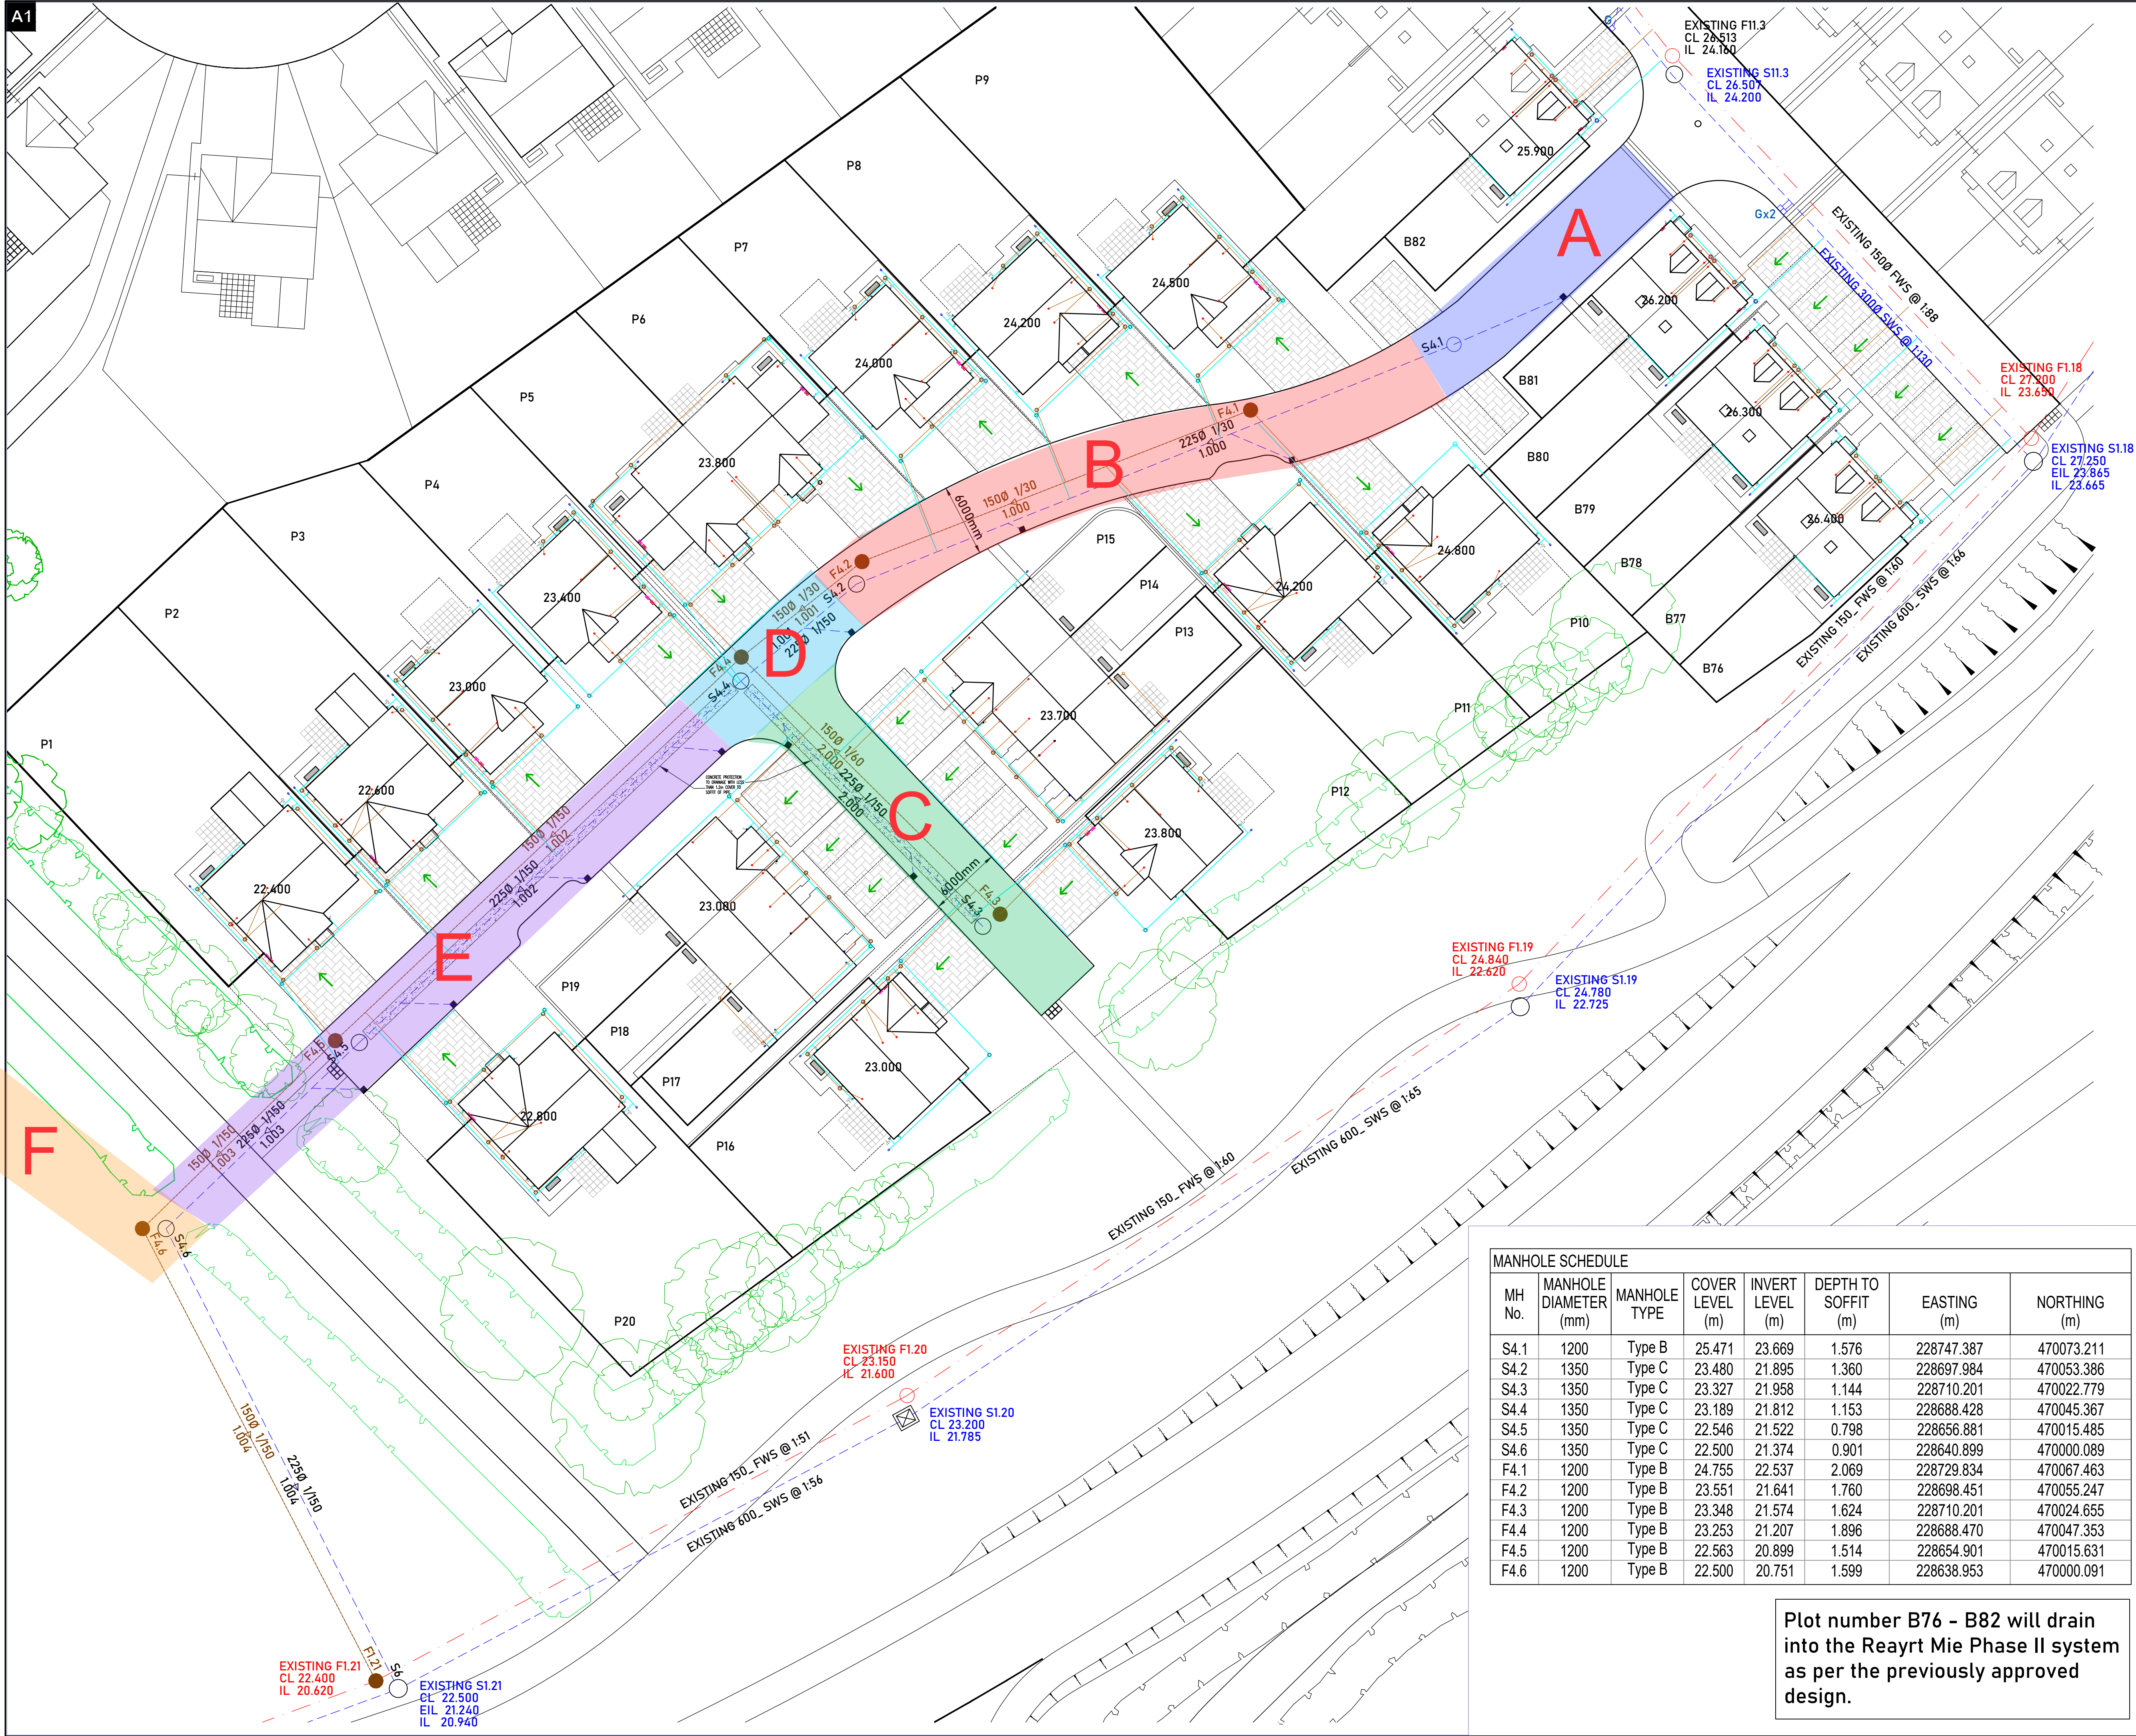

NOTES.

|      |                                            |            |    |
|------|--------------------------------------------|------------|----|
| P02  | Issued for Section 4 & Section 8 Agreement | 09.12.2025 | MS |
| REV. | AMENDMENT                                  | DATE       | BY |

dandara

Dandara Group Head Office  
Isle of Man Business Park  
Coolil Road, Braddan  
Isle of Man  
IM2 2SA  
Tel: 01624 693300 Email: isleofman@dandara.com Web: www.dandara.com

CLIENT:  
Dandara Homes Ltd

PROJECT:  
Parkfield  
Ballahick Lane  
Ballasalla

DRAWING:  
Drainage Layout

STATUS:  
Approval

|                                           |                        |
|-------------------------------------------|------------------------|
| SCALE:<br>1:100                           | DATE:<br>December 2025 |
| JOB No:<br>2333                           | NAME:<br>MS / MK       |
| DRAWING No.:<br>2333-DAN-BA4-DR-D-C-90001 | Rev<br>P02             |

MANHOLE SCHEDULE

| MH No. | MANHOLE DIAMETER (mm) | MANHOLE TYPE | COVER LEVEL (m) | INVERT LEVEL (m) | DEPTH TO SOFFIT (m) | EASTING (m) | NORTHING (m) |
|--------|-----------------------|--------------|-----------------|------------------|---------------------|-------------|--------------|
| S4.1   | 1200                  | Type B       | 25.471          | 23.669           | 1.576               | 228747.387  | 470073.211   |
| S4.2   | 1350                  | Type C       | 23.480          | 21.895           | 1.360               | 228697.984  | 470053.386   |
| S4.3   | 1350                  | Type C       | 23.327          | 21.958           | 1.144               | 228710.201  | 470022.779   |
| S4.4   | 1350                  | Type C       | 23.189          | 21.812           | 1.153               | 228688.428  | 470045.367   |
| S4.5   | 1350                  | Type C       | 22.546          | 21.522           | 0.798               | 228656.881  | 470015.485   |
| S4.6   | 1350                  | Type C       | 22.500          | 21.374           | 0.901               | 228640.899  | 470000.089   |
| F4.1   | 1200                  | Type B       | 24.755          | 22.537           | 2.069               | 228729.834  | 470067.463   |
| F4.2   | 1200                  | Type B       | 23.551          | 21.641           | 1.760               | 228698.451  | 470055.247   |
| F4.3   | 1200                  | Type B       | 23.348          | 21.574           | 1.624               | 228710.201  | 470024.655   |
| F4.4   | 1200                  | Type B       | 23.253          | 21.207           | 1.896               | 228688.470  | 470047.353   |
| F4.5   | 1200                  | Type B       | 22.563          | 20.899           | 1.514               | 228654.901  | 470015.631   |
| F4.6   | 1200                  | Type B       | 22.500          | 20.751           | 1.599               | 228638.953  | 470000.091   |

Plot number B76 - B82 will drain into the Reayrt Mie Phase II system as per the previously approved design.