


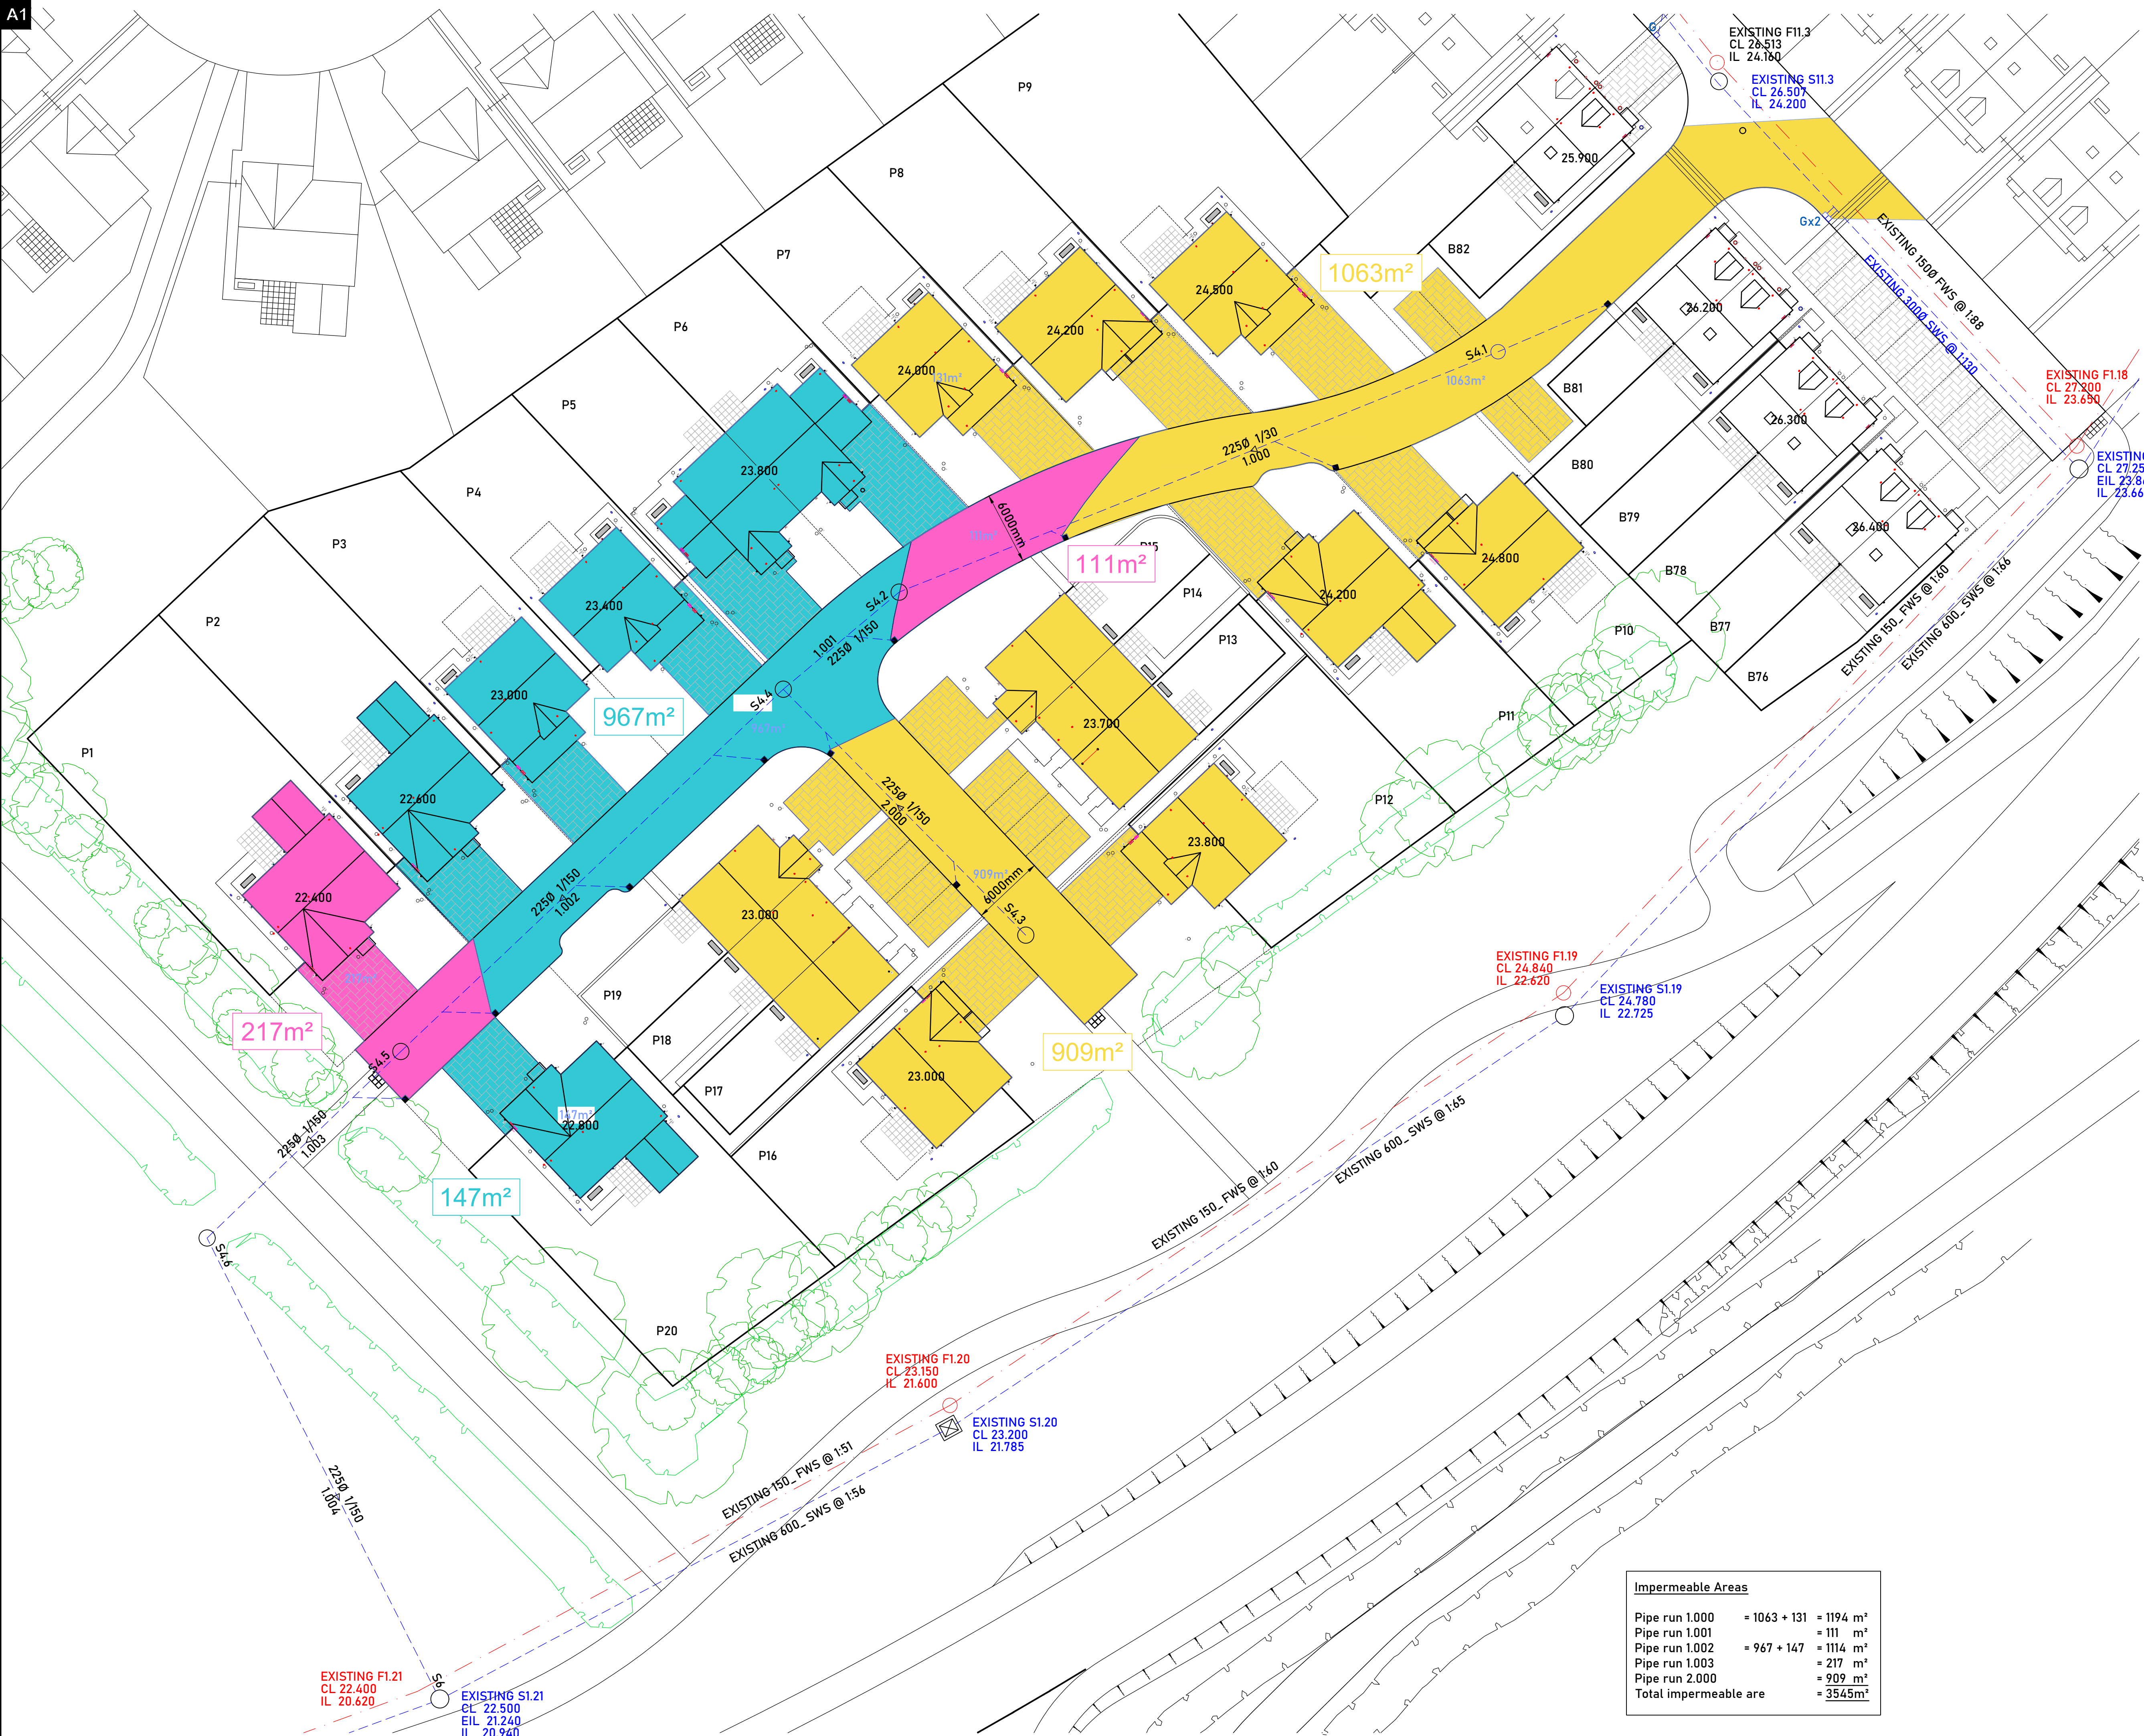

NOTES.

P02	Issued for Section 4 & Section 8 Agreement	09.12.2025	MS
REV.	AMENDMENT	DATE	BY



Dandara

Dandara Group Head Office
Isle of Man Business Park
Cool Road, Braddan
Isle of Man
IM2 2SA

Tel: 01624 693300 Email: isleofman@dandara.com Web: www.dandara.com

CLIENT:

Dandara Homes Ltd

PROJECT:

Parkfield
Ballahick Lane
Ballasalla

DRAWING:

Impermeable Areas

STATUS:

Approval

SCALE:	DATE:
1:100	December 2025

JOB No:	NAME:
2333	MS / MK

DRAWING No.:	Rev
2333-DAN-BA4-DR-D-C-90004	P02